

Diagrama Esquemático da Zona de Mistura

FD = 579:1 | Zona esquemática conforme CONAMA 430/2011 (Art. 13) | Não representa zona regulatória formal

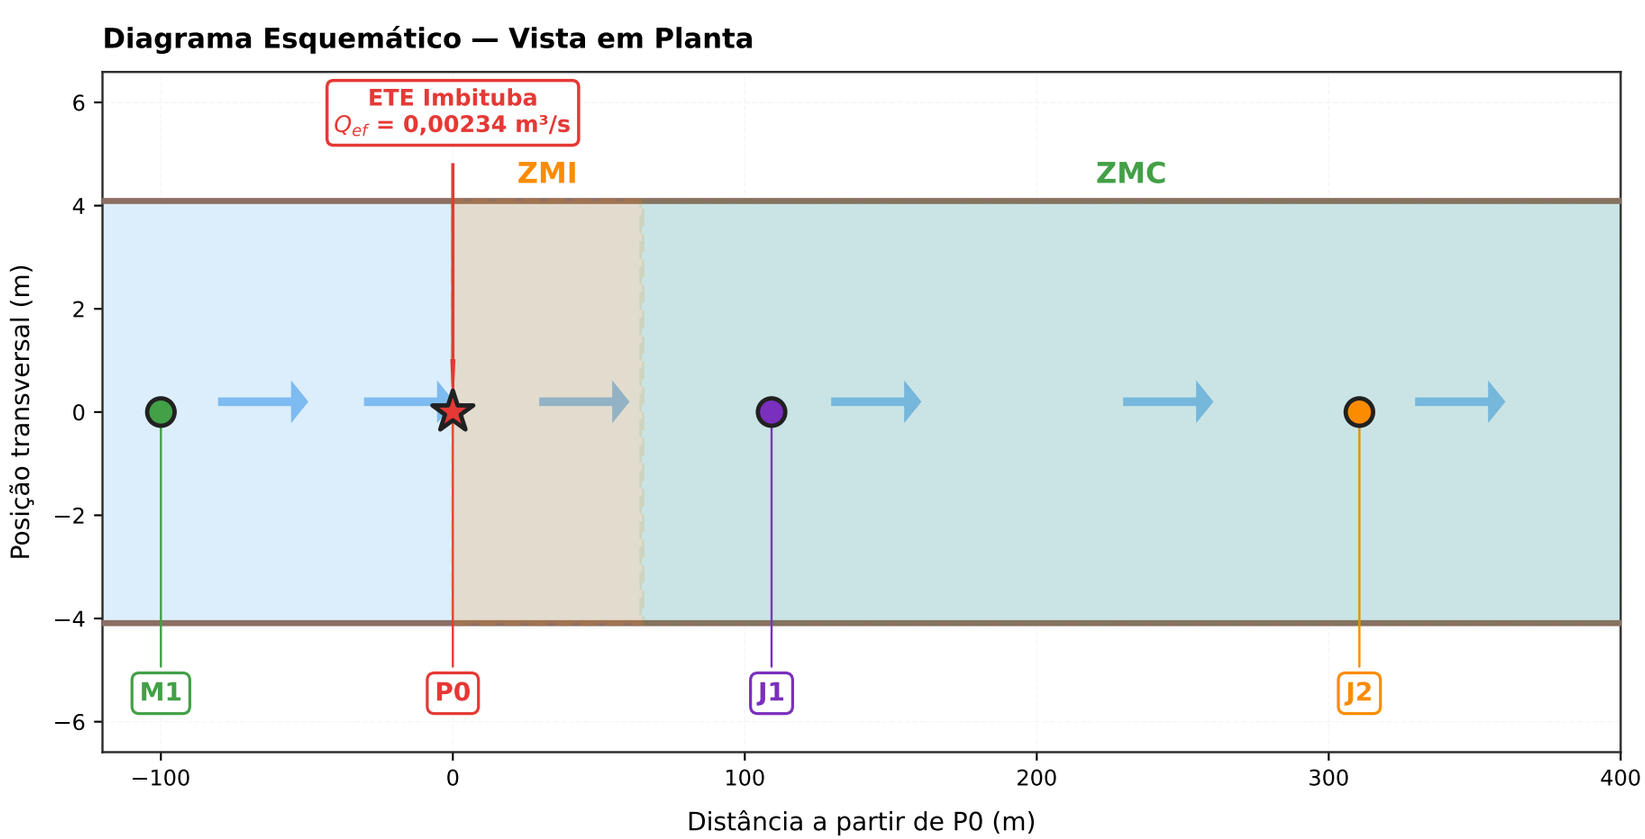

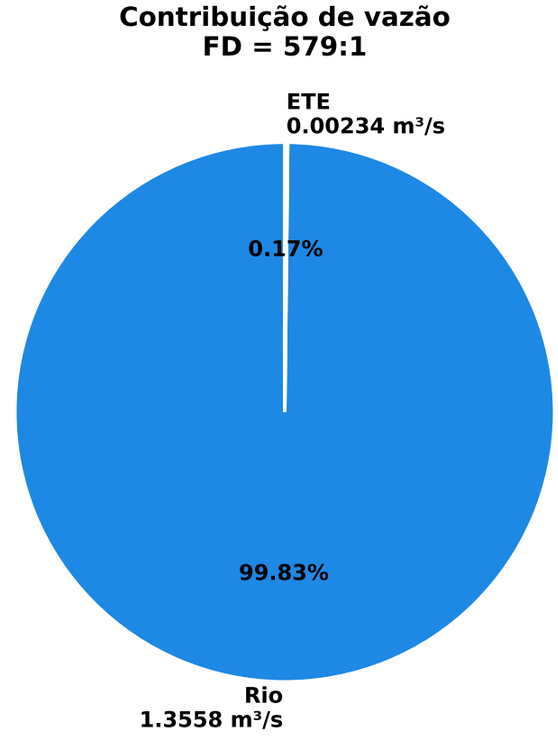

Parâmetro	M1 (rio)	ETE	Pós-mistura	Padrão C2	Situação
DBO5	20.40	22.40	20.403	5.00	⚠ Pré-existente
P-total	0.08	3.02	0.085	0.10	✓ Conforme
NTK	0.64	1.98	0.642	2.00	✓ Conforme